

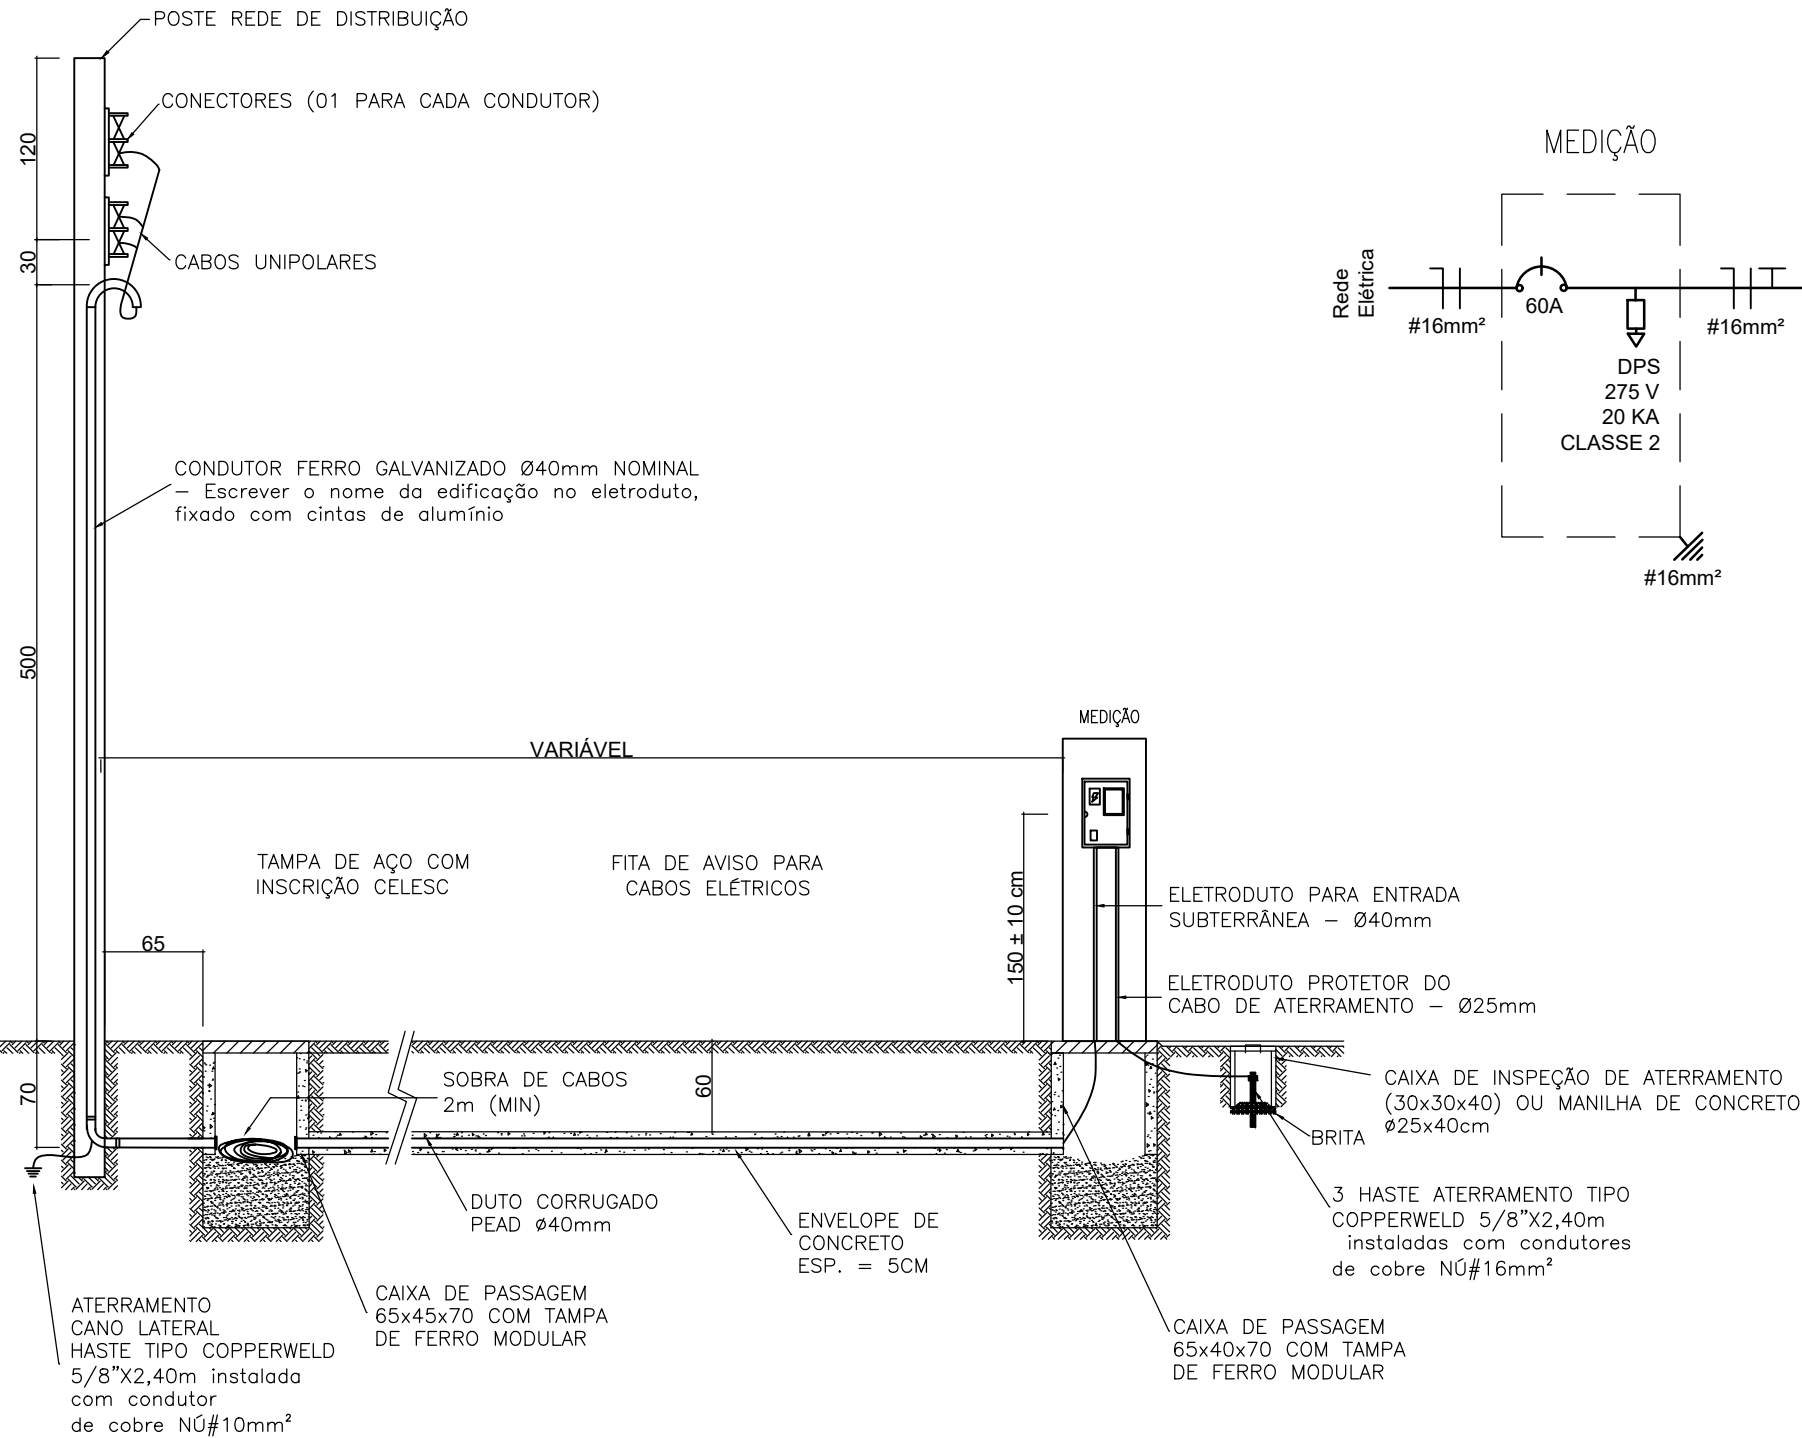


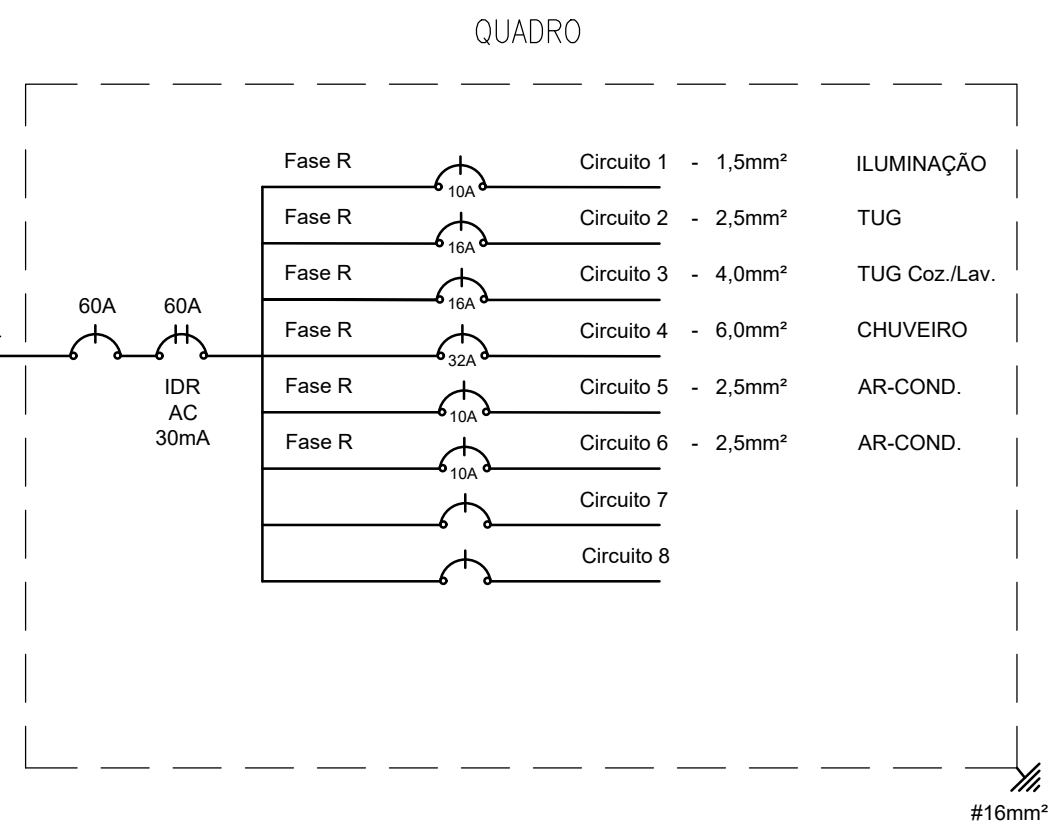

2 ENTRADA DE ENERGIA ELÉTRICA
ESCALA 1:50

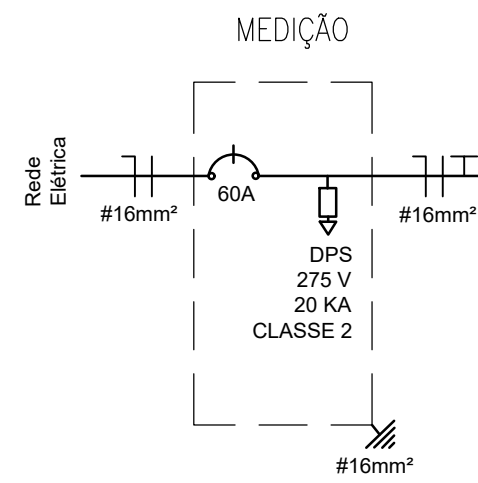

3 DIAGRAMA UNIFILAR
SEM ESCALA

UFSC	Conteúdo: Detalhe da entrada e Diagrama Unifilar			Data: 30/06/2026
	Aluno: Anthony Gabriel Stürmer			Turma: 02202A
EGR 5619	Escala: INDICADA	Unidade: cm	Prof: Deivis Marinoski	Folha: 2/2