


Projeção cobertura / calçada

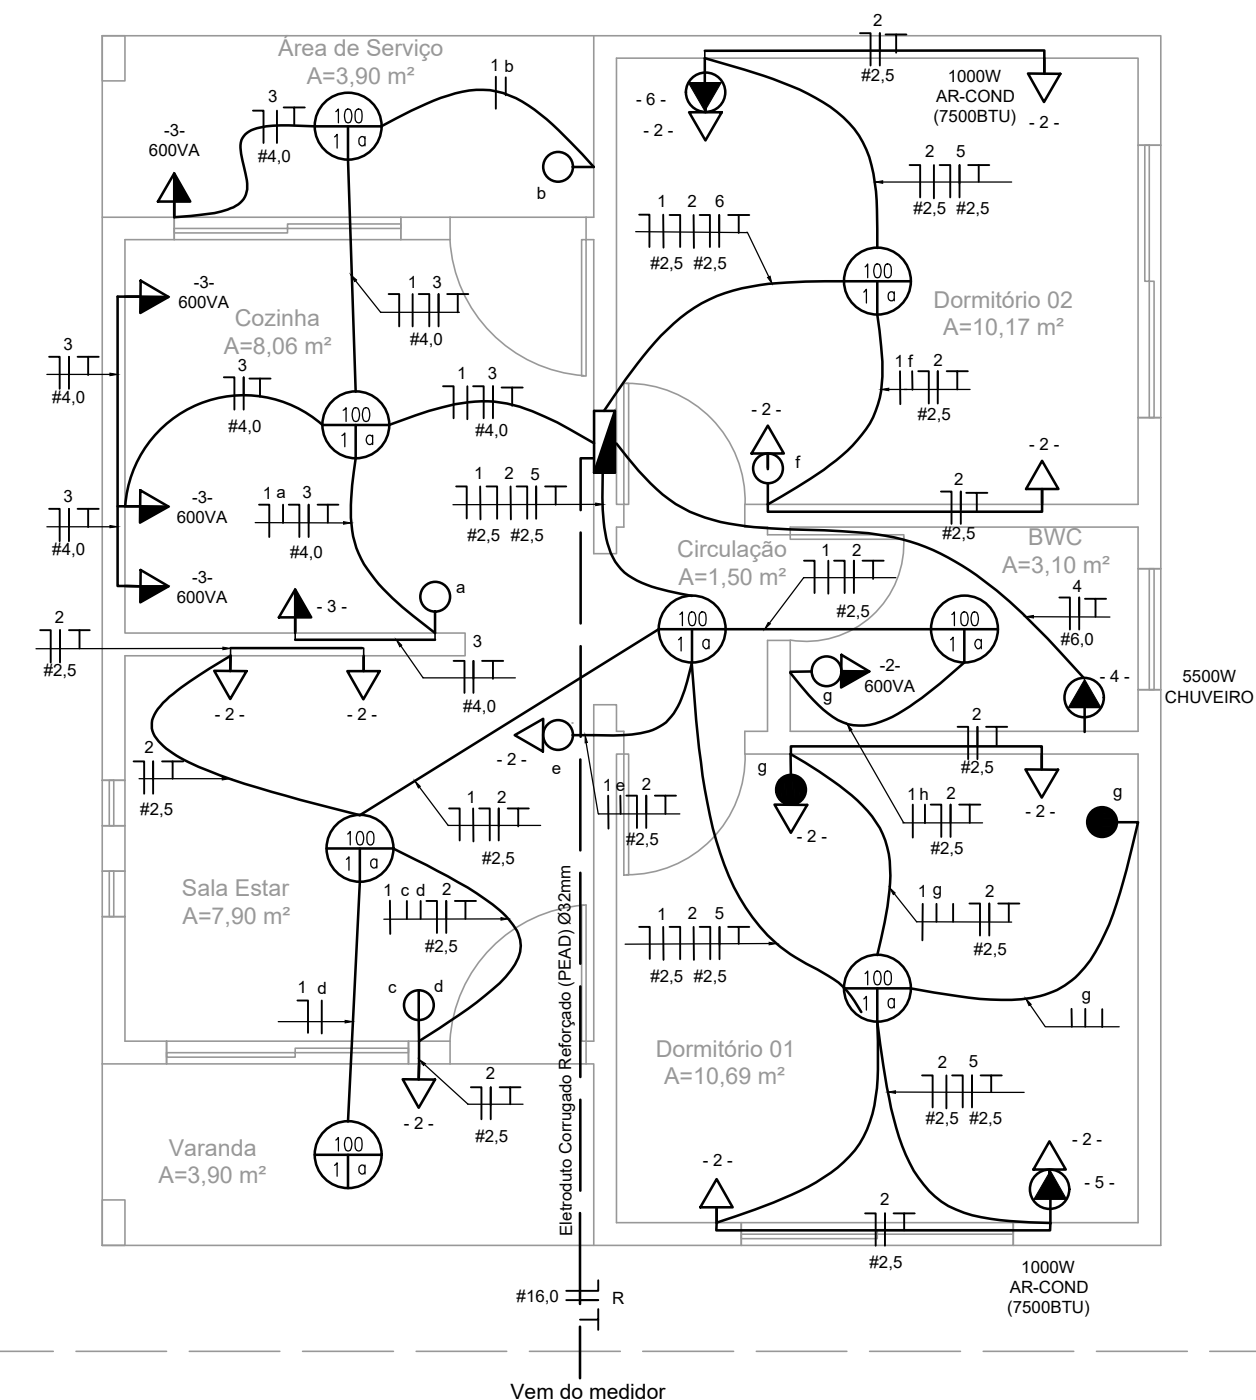

PLANTA BAIXA

1

NOTAS


1. Eletrodutos não cotados são de PVC flexível Ø25mm nominal.
2. Eletrodutos enterrados são do tipo PEAD.
3. Fiação não cotada é de #1,5mm².
4. Fiação interna isolamento 750V.
5. Tomadas sem indicação são de 100W.

6. Todas as tomadas devem ser aterradas.
7. Condutor de aterramento deverá ser igual ao condutor fase respeitando mínimo de #2,5mm².
8. Áreas molhadas usar cabos com isolamento 1kV
9. Altura dos interruptores = 1,20m do piso acabado na posição vertical.

10. Tensão de alimentação 220V.
11. Adotar as seguintes cores para os condutores

Terra = verde
Neutro = azul claro
Fase = vermelha
Retorno = preta

SIMBOLOGIA

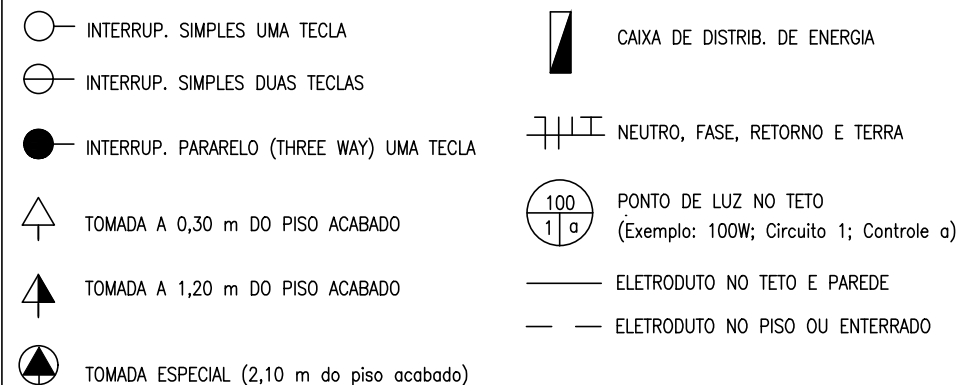

QUADRO DE PREVISÃO DE CARGAS

QUADRO DE PREVISÃO DE CARGAS										
Dependência (ambiente)	Dimensões		Iluminação			T.U.G.			T.U.E.	
	Área (m²)	Perímetro (m)	Nº pontos	Potência Unit. (W)	Potência Total (W)	Nº pontos	Potência Unit. (W)	Potência Total (W)	Aparelho	Potência (W)
Varanda	3.90	8.90	1	100	100	1	100	100		
Sala de Estar	7.90	11.30	1	100	100	3	100	300		
Cozinha	8.06	11.40	1	100	100	1	100	100		
						3	600	1800		
Dormitório 01	10.69	13.10	1	160	160	4	100	400	Ar-Cond.	1000
Dormitório 02	10.17	12.80	1	160	160	4	100	400	Ar-Cond.	1000
BWC	3.10	7.30	1	100	100	1	600	600	Chuveiro	5500
Circulação	1.50	5.00	1	100	100	0		0		
Área de Serviço	3.90	8.90	1	100	100	1	600	600		
TOTAIS			8		920	18		4300	3	7500

QUADRO DE CARGAS

QUADRO DE CARGAS										
Circ.	Circuito Tipo/local	Carga	Carga	Carga	Carga	Tensão	Corrente	Disj	Cond	Fase
Nº		Ilum. (W)	T.U.G. (W)	T.U.E. (W)	Total (W)	(V)	(A)	(A)	(mm²)	
1	Iluminação	920			920	220	4.2	10	1.5	R
2	Tomadas		1800		1800	220	8.2	16	2.5	R
3	Tomadas Coz-Lav		2500		2500	220	11.4	16	4.0	R
4	Chuveiro			5500	5500	220	25.0	32	6.0	R
5	Ar-Cond.		1000	1000	2000	220	4.5	10	2.5	R
6	Ar-Cond.		1000	1000	2000	220	4.5	10	2.5	R
7	Reserva									
8	Reserva									
TOTAL					12720	220	57.8	60	16.0	R

UFSC

EGR 5619

Conteúdo:
Projeto Elétrico Residencial - Planta baixa e Quadros

Aluno:
Anthony Gabriel Stürmer

Escala:
1:50

Unidade:
cm

Prof:
Devis Marinoski

Data:
15/06/2026

Turma:
02202A

Folha:
1/2